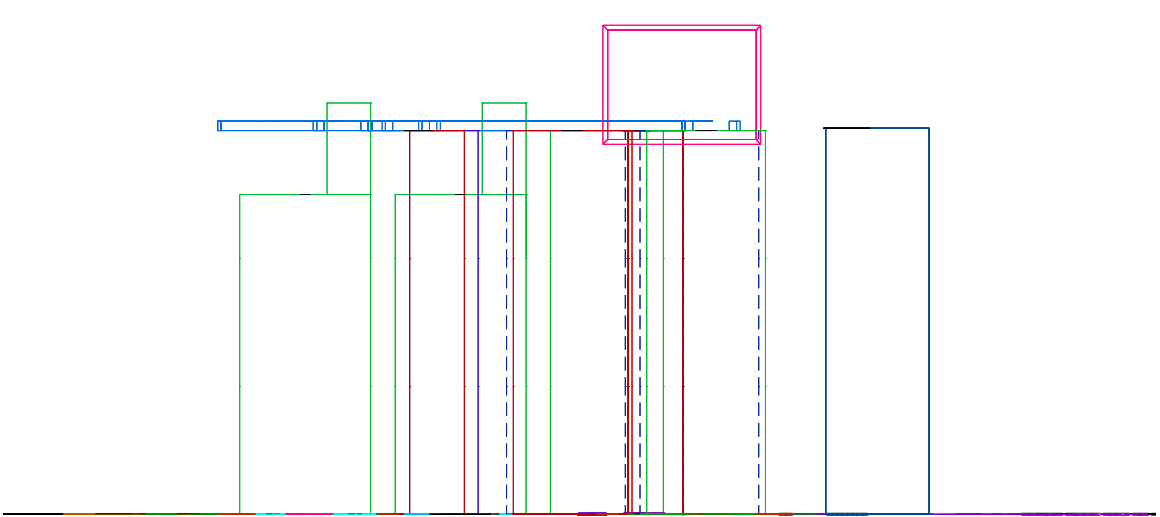
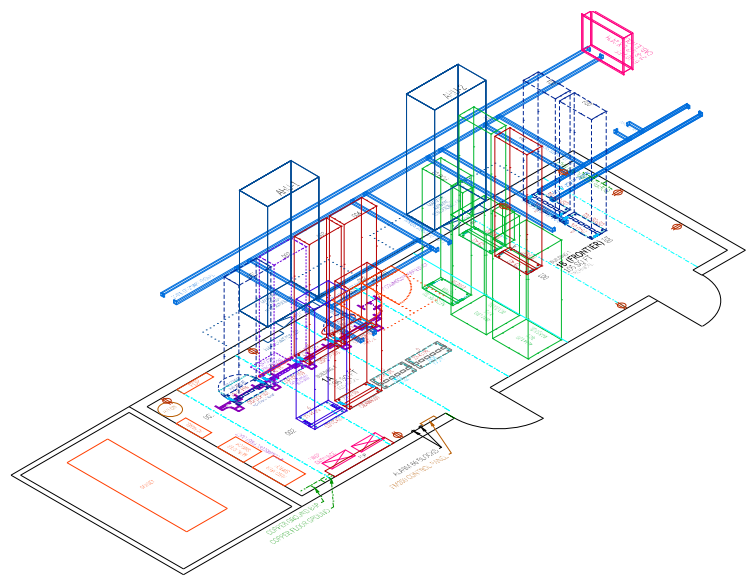
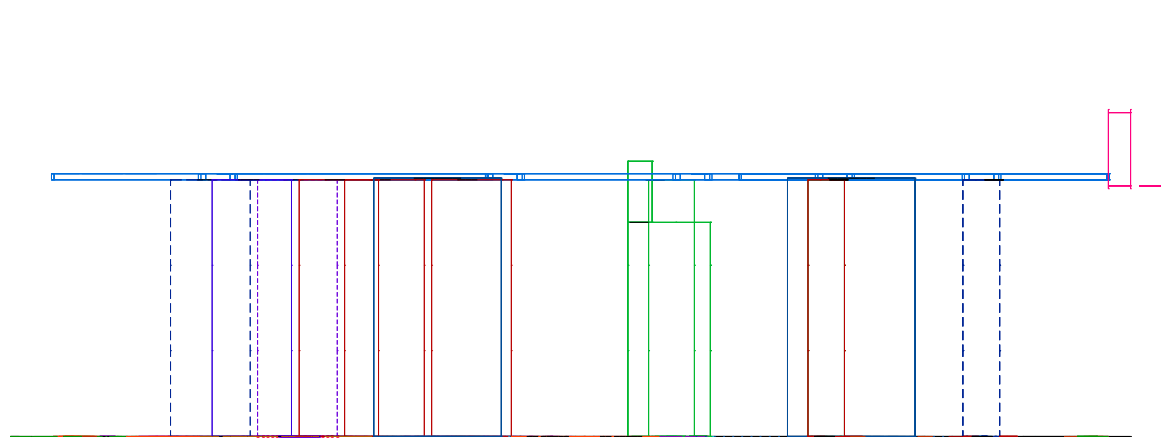
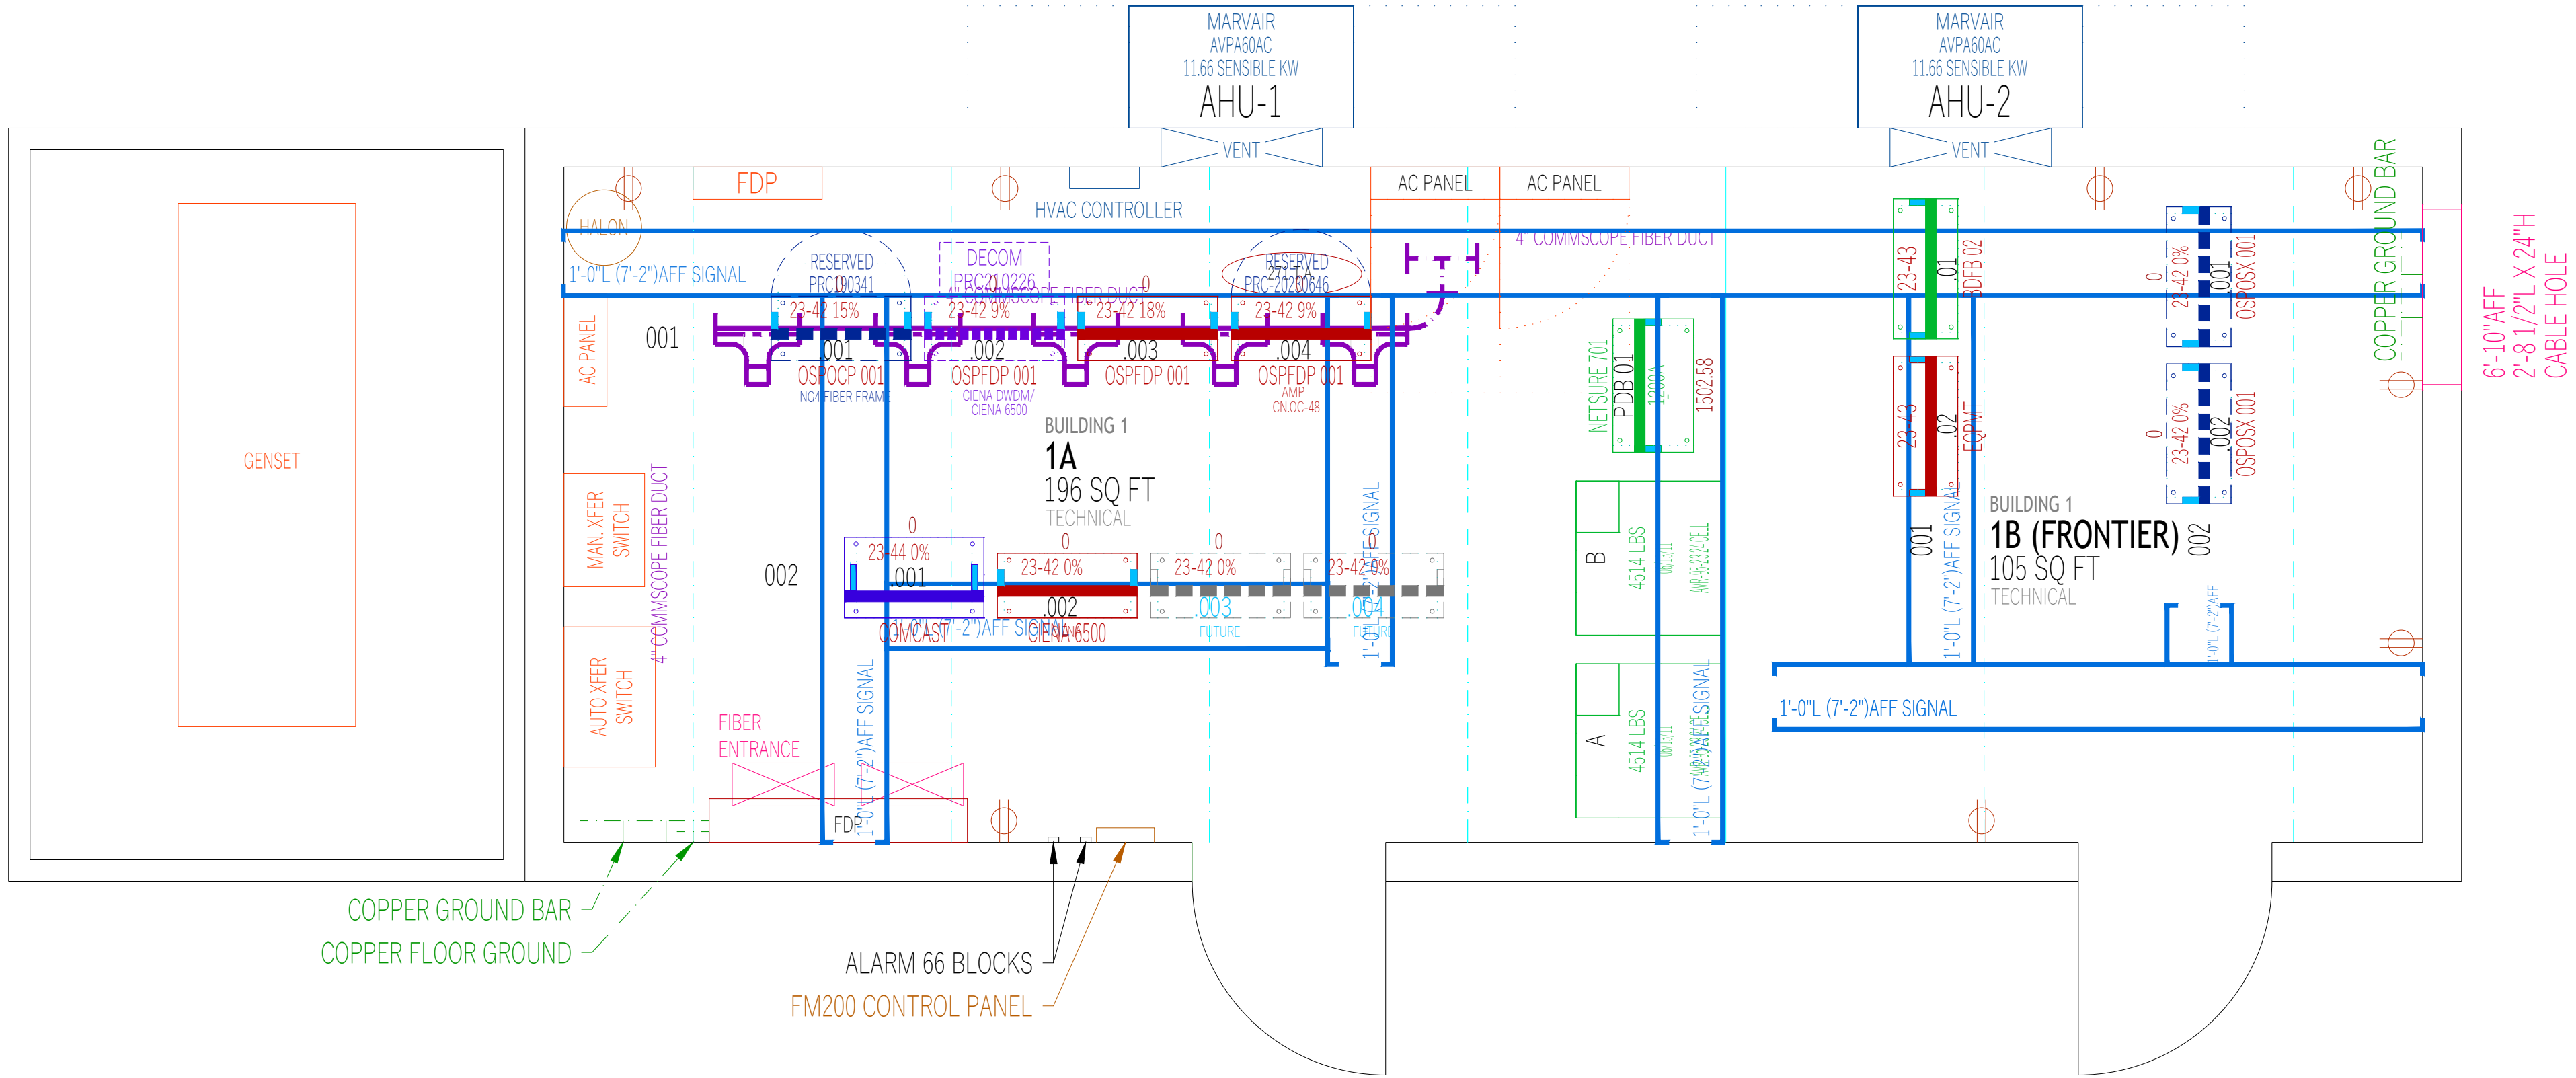


VERSIONS					
VERSION: 1	DATE: 26Sep18	ENG:	PM:	[DRAFT: Auto]	
CREATED FROM DGN FILE(S) IN AUTOMATED PROCESS: 488200001.dgn, 488100001.dgn					
VERSION: 2	DATE: 5AUG19	ENG: TD	PM: EJ	[DRAFT: CH]	
RESERVE RR0101.01 AS NG4 FIBER FRAME PER PRC-2019-0341					
VERSION: 3	DATE: 22JUL20	ENG: TD	PM: EJ	[DRAFT: CH]	
RESERVE RR0102.01 COMCAST PER PRC2020-0329					
VERSION: 4	DATE: 24MAY21	ENG: WR	PM: EJ	[DRAFT: CH]	
DECOM SPACE & POWER DECOMMISSION FOR CIENA CORESTREAM ULI1 WTU103. EQUIP RR 0102.02 PER PRC2021-0226					
VERSION: 5	DATE: 23NOV22	ENG: JPM	PM: JAF	[DRAFT: JPM]	
ADD 4" FIBER DUCT AND DROPS PER MADISON AS-BUILTS. W/O # CSRKCOCF-IN-Fiberduct-01. CSS # N/A. N614026					
VERSION: 6	DATE: 16NOV23	ENG: SF	PM: SF	[DRAFT: KWW]	
RR0101.04 CSRKCOCFH00PLT1 FED BY POWER BAY EQUIP ROOM BLDG 1, PANEL A1 & B1, POSITION 12 EA (30A AUG TO 40A). PRC-2023-0610					
VERSION: 7	DATE: 13DEC23	ENG: SF	PM: SF	[DRAFT: KWW]	
PLEASE CANCEL PRC2023-0610(BREAKER SWAP) AND PROCESS PRC2023-0644(ADDITIONAL 20A) RR0101.04 CSRKCOCFH00PLT1 FED BY POWER BAY EQUIP ROOM BLDG 1, PANEL A1 & B1, POSITION 12 EA (30A AUG TO 40A). PRC-2023-0610 R1. RR0101.04 CSRKCOCFH00PLT1 FED BY POWER BAY EQUIP ROOM BLDG 1, PANEL A1 & B1, POSITION 13 EA (20A). PRC-2023-0646					
VERSION: 8	DATE: 18Feb2025	ENG: CC	PM: CC	[DRAFT: CC]	
ADDING 2 NG4 SKINNY DESIGNATIONS TO EMPTY, EXISTING RACKS IN BUILDING 1B FOR 1152 FIBER ADD UNDER PROJ. TITANIUM. SPOKE WITH TONY D AND SABY. NO PRC NEEDED. N618423					
VERSION: 9	DATE: 28JUL25	ENG:	PM: LC	[DRAFT: AEV]	
PLACED (2) NG4 SKINNY FRAMES FOR TITANIUM PROJECT TO FACILITATE 1152 FIBER. WO23096					
VERSION: 10	DATE: 05SEP25	ENG: AP	PM: SF	[DRAFT: SF]	
REPLACE 2 x FAILED DEKA AVR95-23 BATTERY STRINGS LIKE FOR LIKE IN EXISTING STANDS. UPGRADE DC PLANT NETSURE 701 CONTROLLER TO NOU. N663569					
VERSION: 11	DATE: 19NOV25	ENG:	PM:	[DRAFT: KWW]	
UPDATE BLOCKS WITH PRO DATA AND UPDATE LAYERS AND PAPERSPACE LAYOUT.					

LUMEN®

INFORMATION IN THIS DOCUMENT IS PROPRIETARY AND SHALL NOT BE USED, COPIED, REPRODUCED, OR DISCLOSED IN WHOLE OR IN PART WITHOUT WRITTEN CONSENT OF LUMEN TECHNOLOGIES, LLC.					
APPROVAL 1:		DATE:	GLJI CODE/ADDRESS:		
DRAWN BY:		CSRKCOCF			
		Play = 0			
KWW Automated		182 PRAIRIE HWY. CR @ MP 70512 BNSF CASTLE ROCK, CO			
SIZE:	DRAWING TITLE:				
D	FLOOR PLAN - 488				
CEILING HGT:		DRAWING NUMBER:			REVISION:
?		CSRKCOCF-FP-01-01-CN			11
SCALE:		RELEASED:			
1/2"=1'		11/19/25		SHEET:	
				1 OF 1	