
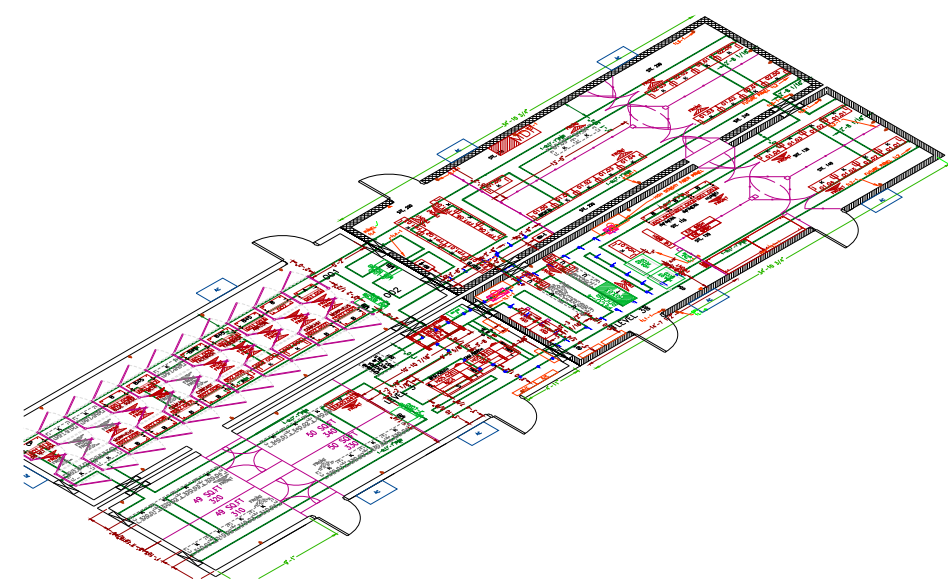


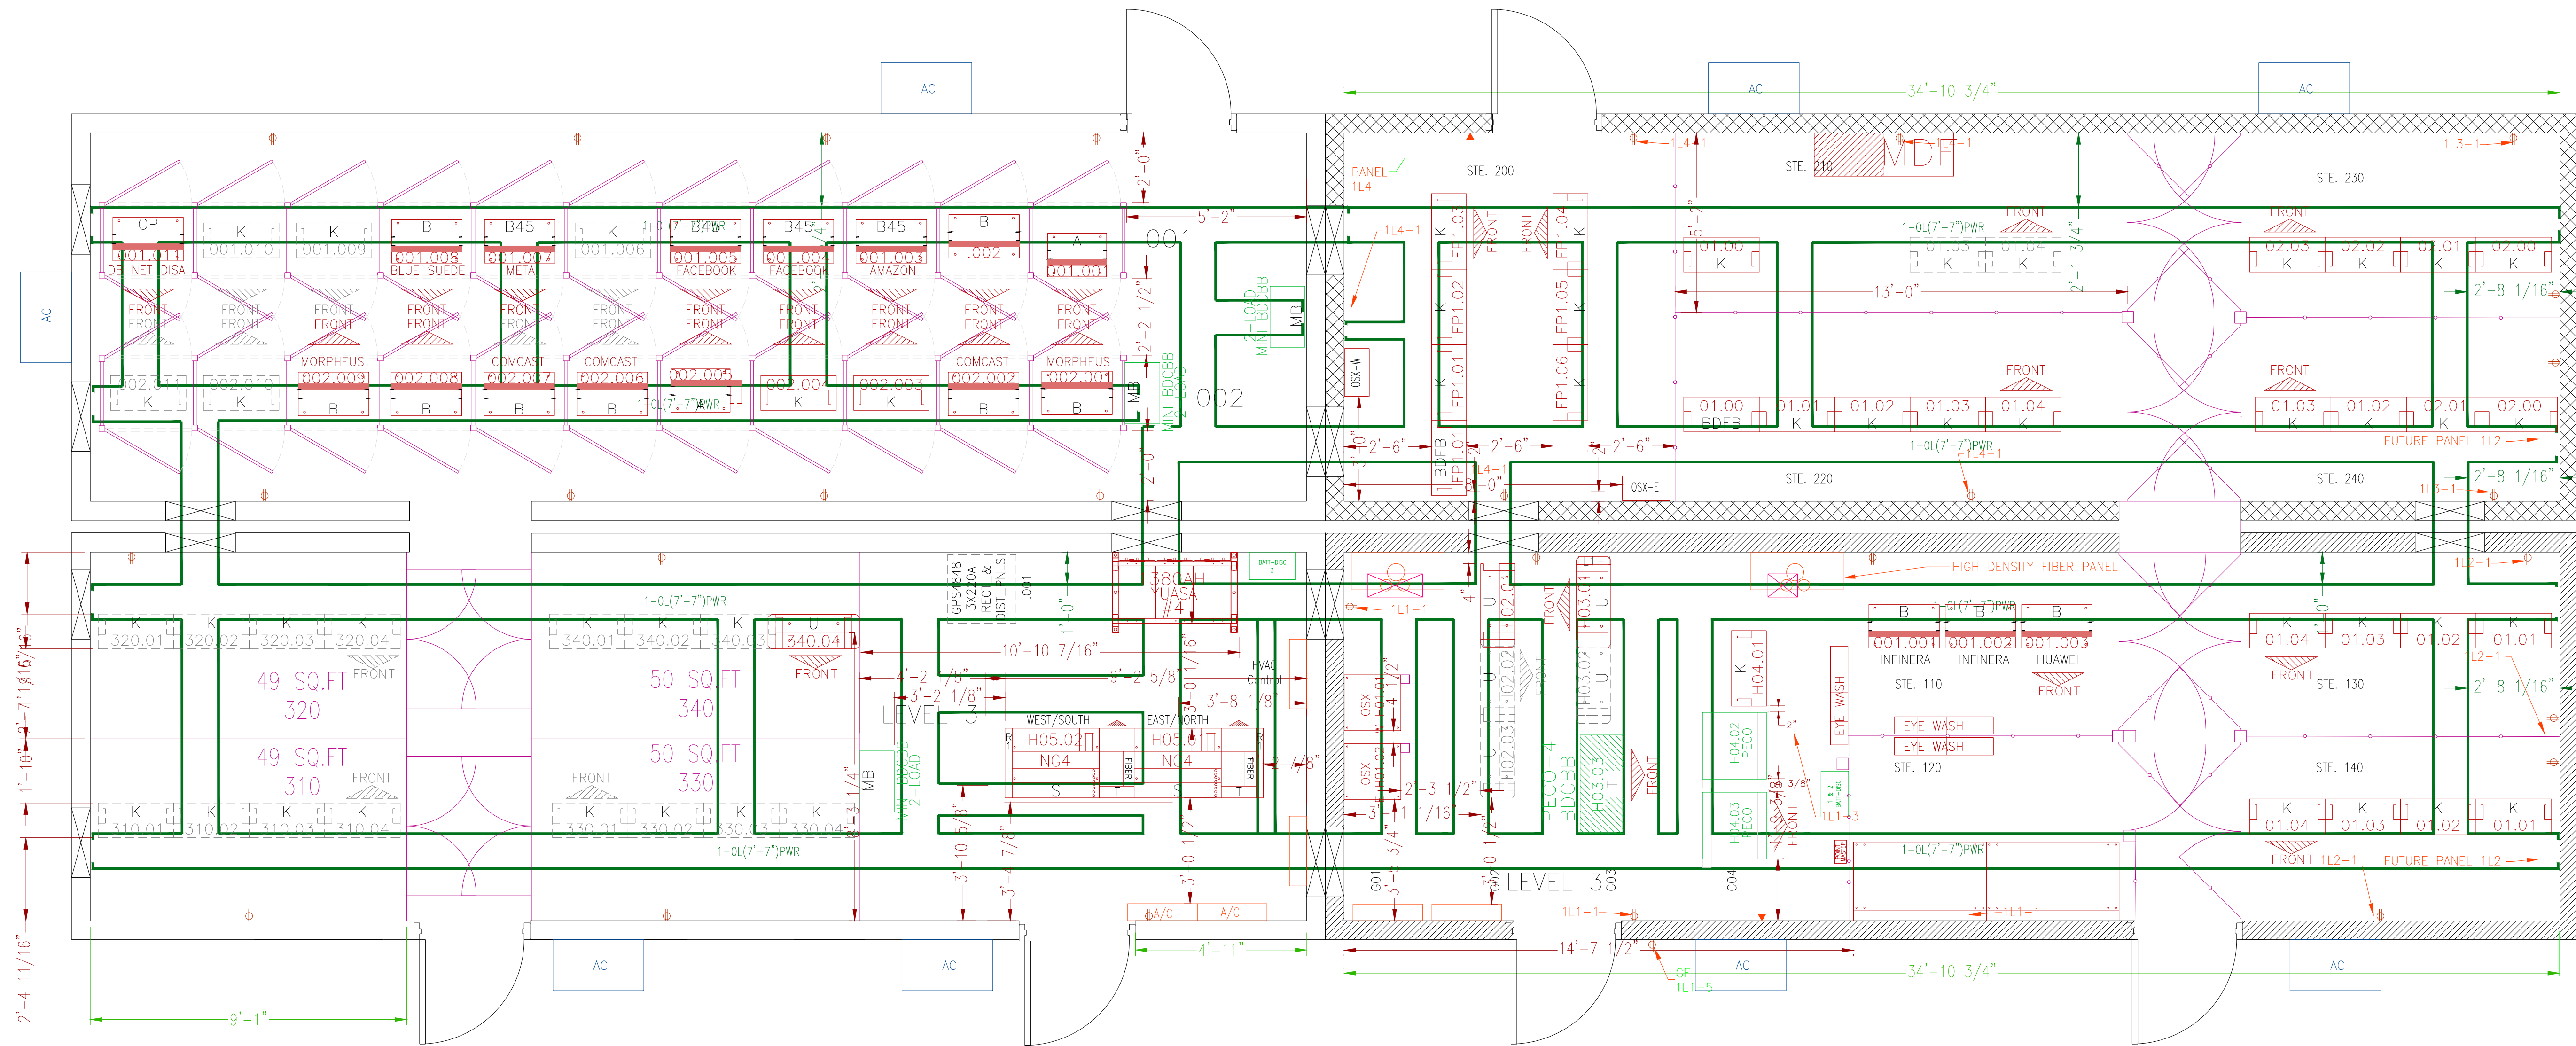

FRONT

ISO

RIGHT

VERSIONS					
VERSION: 13	DATE: 7NOV17	ENG:	PM: KWW	DRAFT: dp	
ADDED NEW TITLE BLOCK AND UPDATED LAYERS TO NEW STANDARD					
VERSION: 14	DATE: 27NOV17	ENG: JPM	PM: JAF	DRAFT: JPM	
ADDED (1) 23" CHANNEL RELAY RACK IN HUT 4, ICC 002.002 (420.02) FOR COMCAST UNICORN. WO# PTVLC003-COI-UNICORN-01 CSS# COMCAST20L3ILA N379030					
VERSION: 15	DATE: 16JUL18	ENG: JPM	PM: JAF	DRAFT: JPM	
ADDED (1) 23" 45RU CHANNEL RELAY RACK IN HUT 4, ICC 001.004 (410.04) FOR FACEBOOK. WO# PTVLC003-COI-FACEBOOK-01 CSS# FACBK50FPL3RLNRF45RU N420528					
VERSION: 16	DATE: 13JAN19	ENG: JPM	PM: JAF	DRAFT: JPM	
INSTALL (1) 23" 45RU CHANNEL RELAY RACK IN HUT 4, ICC CAGE 001.005 (410.05) FOR FACEBOOK. WO# PTVLC003-COI-FACEBOOK-02 CSS# FACBK60FPL3RLNRF45RU N457318					
VERSION: 17	DATE: 13JAN19	ENG: JPM	PM: JAF	DRAFT: JPM	
INSTALL (1) 23" 45RU CHANNEL RELAY RACK IN HUT 4, ICC CAGE 001.003 (410.03) FOR AMAZON. WO# PTVLC003-COI-AMAZON-01 CSS# AMAZON20FPL3RLNRF45RU N464387					
VERSION: 18	DATE: 05APR24	ENG: JPM	PM: JAF	DRAFT: JPM	
INSTALL (1) 23" 45RU CHANNEL RELAY RACK IN HUT 4, ICC CAGE 001.007 (410.07) FOR META. WO# PTVLC003-COI-METAR&P-01 CSS# FACBK60TRIMFPL3RLNRF N877308					

LUMEN®

INFORMATION IN THIS DOCUMENT IS PROPRIETARY AND SHALL NOT BE USED, COPIED, REPRODUCED, OR DISCLOSED IN WHOLE OR IN PART WITHOUT WRITTEN CONSENT OF LUMEN TECHNOLOGIES, LLC.

APPROVAL 1:	DATE:	CLIENT CODE/ADDRESS:
DRAWN BY:		PTVLC003 1ST FLOOR 12616 WELD COUNTY ROAD 28 PLATTEVILLE, CO
SIZE:	DRAWING TITLE:	
D	ILA	
CEILING HGT:	DRAWING NUMBER:	REVISION:
	PTVLC003-FP-01-01-L3	18
SCALE:	RELEASED:	SHEET:
3/8"=1'	7NOV17	1 OF 1